



04 TENDER S.U.R.E.

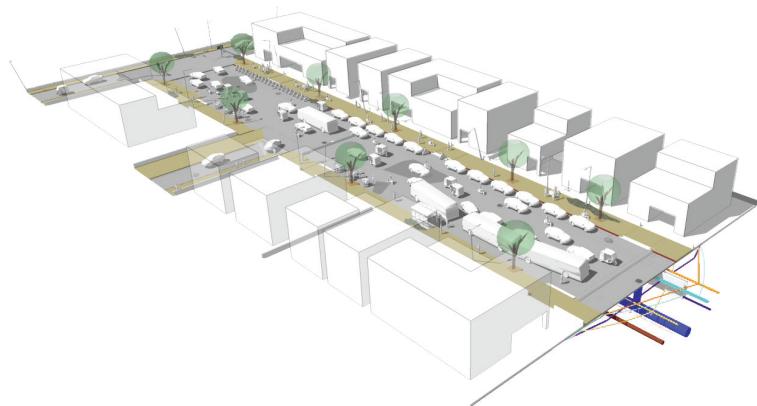

STANDARD ROAD
BEFORE TENDER S.U.R.E.




STANDARD ROAD
AFTER TENDER S.U.R.E.

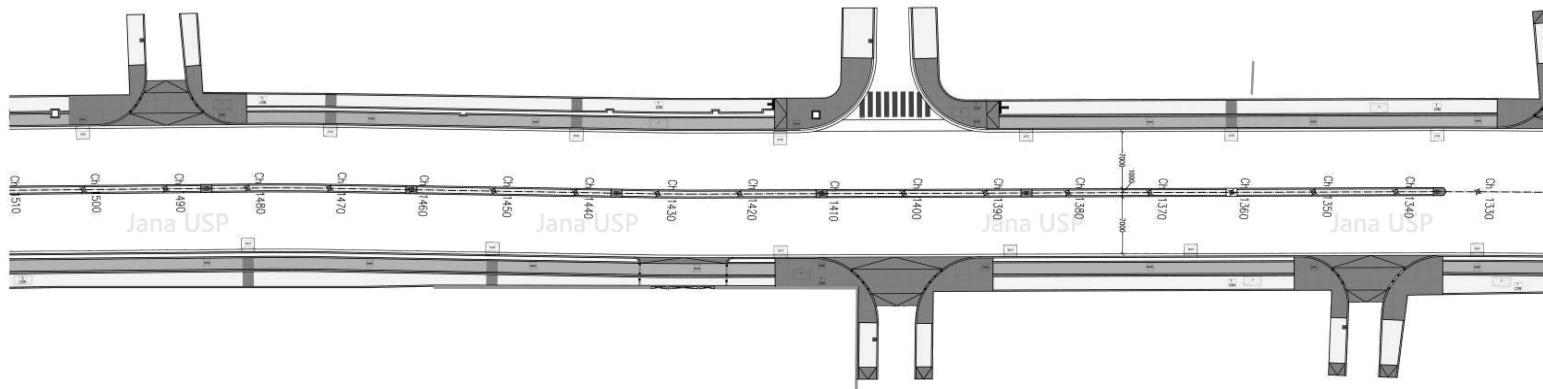

SURFACE DESIGN PLAN

WORKING DRAWING

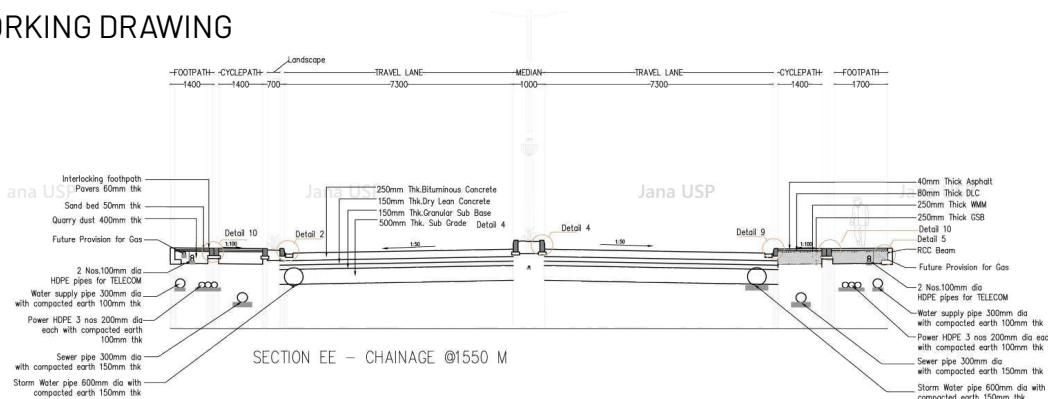

CROSS SECTION WORKING DRAWING

PHASE 3 ALIGNMENT & SURFACE DESIGN FOR CBD ROADS

Project Role: Associate

Team Size: Studio Project (11 to 13)

PHASE 3 ALIGNMENT & SURFACE DESIGN FOR CBD ROADS

Project Role: Associate

Team Size: Studio Project (11 to 13)

Phase 1 of Tender S.U.R.E. involved the redevelopment of 12 key roads in the Bangalore Central Business District.

Following its success, the State Government announced 50 more roads to be redeveloped under the Tender S.U.R.E. model.

Among the proposals sent by Jana USP, I worked primarily on the design of 3 roads namely:

1. Lavelle Road (1375m)
2. Hayes Road (310m)
3. Convent Road (470m)

Personal involvement in the project:

1. To carry out road surveys and vehicular counts for capacity assessment.

2. Design travel lanes considering the Right-of-Way available.